
| PROJ. REFERENCE: | DRAWING NAME: | | REVISION: | | DRAWN BY: | |
|---|---|---|---|---|---|---|
| TBC | 2F PT LAYOUT PLAN (REDRAFT) | | TBC | | CLAUDE (DRAFT) | N |
| DRAWING NUMBER: | DRAWING STAGE: | CLIENT: | SCALE: | | ISSUE DATE: | |
| TBC | REDRAFT FOR REVIEW | TBC | 1:200 | | 16-OCT-2026 | STRUCTURAL (BIM) |

# 2F POST-TENSION LAYOUT PLAN (REDRAFT) - LEVEL +3.100

SCALE 1:200 | NET AREA = 829.05 SQ.M. (AS SOURCE) | REDRAFT FOR REVIEW - NOT FOR CONSTRUCTION

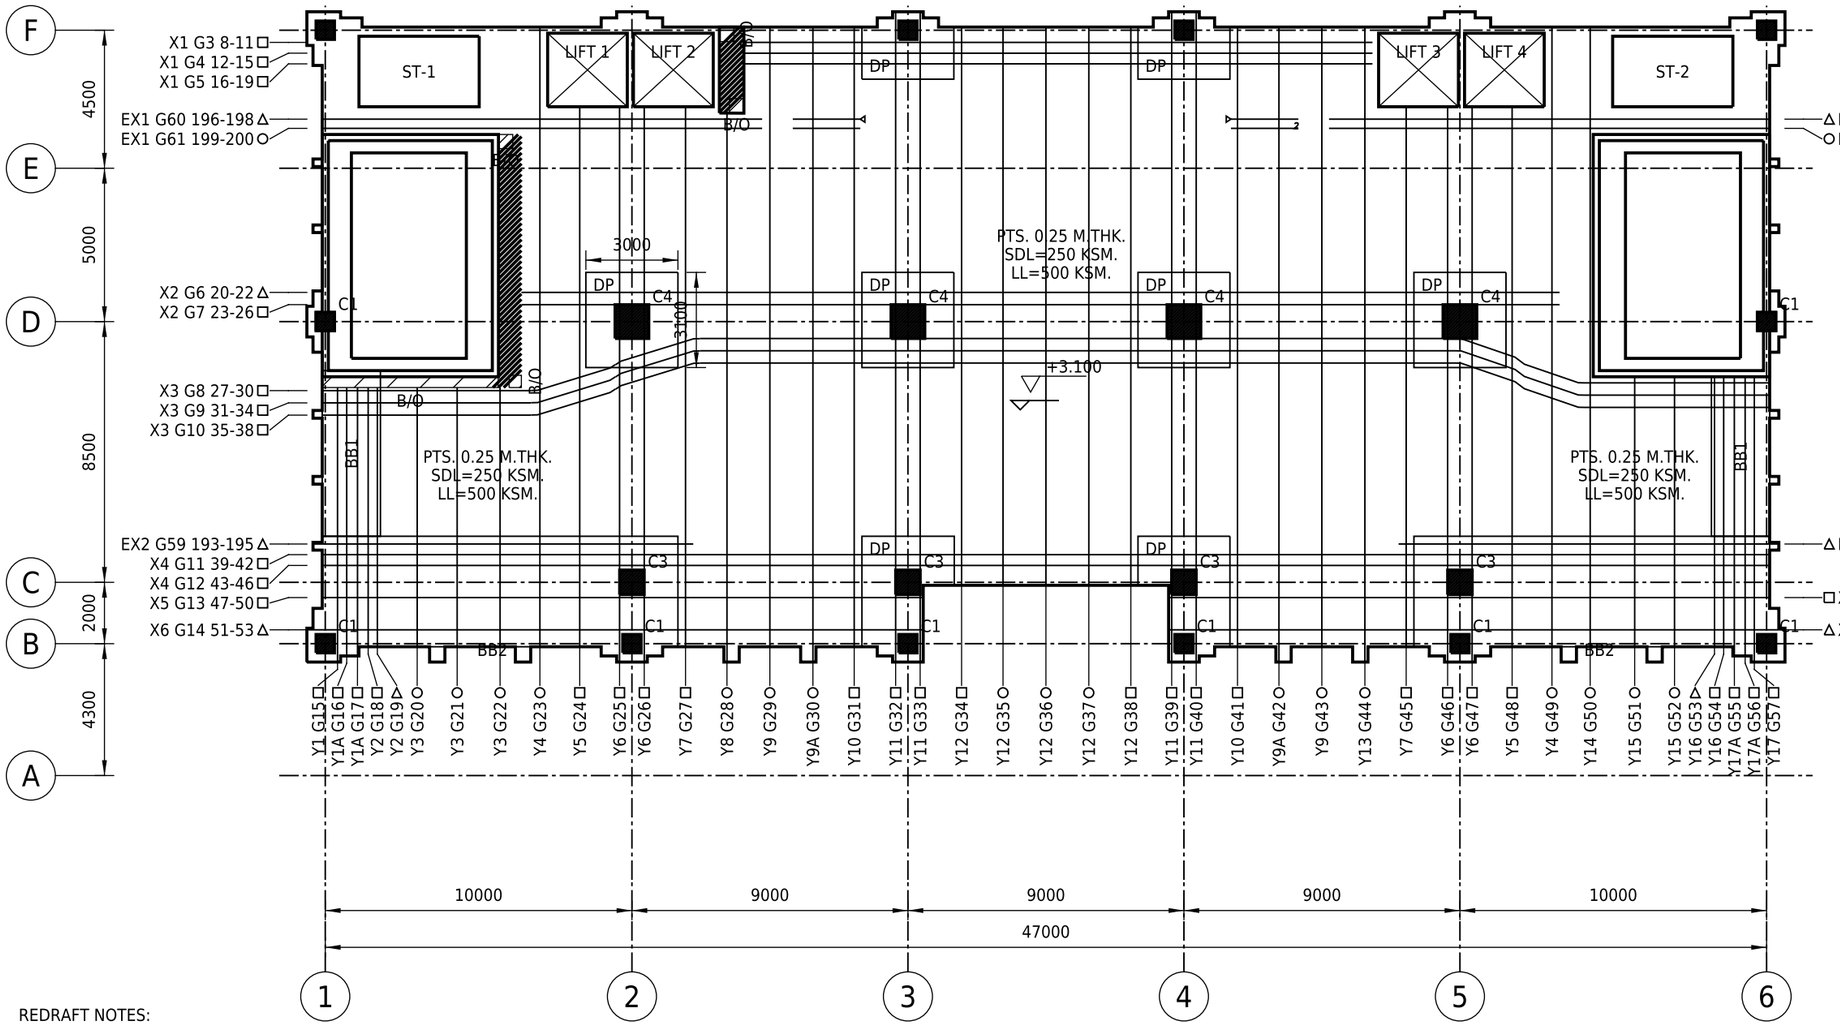


REDRAFT NOTES:

A. REDRAFT FOR REVIEW ONLY - NOT FOR CONSTRUCTION. SOURCE: SUCCESS DESIGN & BUILD CO., LTD, SHEETS 14-16 OF 50, REV 01, 22-AUG-2023.
B. SLAB, WALL, VOID, COLUMN, DROP PANEL AND TENDON GEOMETRY TAKEN FROM THE SOURCE VECTOR DATA (+/-0.3 m). NO DESIGN CHANGE.
C. TENDON MARKS, GROUP NO., STRAND NOS. AND LENGTHS WERE READ FROM THE SOURCE LABELS AND ARE TRANSCRIBED - VERIFY.
D. STRAND COUNT BY SYMBOL: SQUARE = 4, TRIANGLE = 3, CIRCLE = 2 STRANDS. STRESSING / DEAD-END SYMBOLS NOT REDRAWN - TBC.
E. NOT REDRAWN: STAIR TREADS, REINFORCEMENT TABLES, TENDON PROFILES (SOURCE SHEET 16), TYPICAL DETAILS. JACKING FORCE AND LOSSES: TBC.
F. B/O = BLOCKED OUT FOR STRESSING 0.80 m WIDE (SOURCE TEXT SAYS '0.80 CM' - LIKELY TYPO, TBC). HATCHED ON PLAN.
G. DP = DROP PANEL 0.45 M.THK. (3000 x 3100 TYPICAL AT COLUMN LINE D). BB1 / BB2 = BAND BEAM 1 / 2, 0.45 M.THK. CYAN OUTLINES (S-CONC-DROP).
H. COLUMN SIZES FROM SOURCE VECTOR DATA: C1 600 x 600, C3 800 x 800, C4 1100 x 1100 mm. SLAB 0.25 M.THK. (PTS) EXCEPT DP / BB.

SOURCE GENERAL NOTES (TRANSCRIBED FROM SOURCE SHEET - NOT VERIFIED):

1. CONCRETE: MIN. fc' = 32 MPa AT 28 DAYS (CYLINDER). MIN. fci = 24 MPa AT TRANSFER (CYLINDER).
   MIN. CONCRETE COVER TO NEAREST REINFORCEMENT = 20 mm.
2. PRESTRESSING: POST-TENSIONING SLAB DESIGN AND SYSTEM SHALL BE BONDED.
   STRAND 12.7 mm NOMINAL DIA., 7-WIRE, STRESS RELIEVED, LOW RELAXATION TO ASTM A416.
3. REINFORCEMENT: DIA. 12 mm AND LARGER = DEFORMED BARS GRADE SD40, fy = 400 MPa.
   DIA. 9 mm AND 6 mm = ROUND BARS GRADE SR24, fy = 240 MPa.
   TOP REINFORCEMENT NOT TO BE INSTALLED UNTIL AFTER TENDONS HAVE BEEN PLACED.
4. SUPPORT SCAFFOLD UNTIL THE CONCRETE HAS THE COMPRESSIVE STRENGTH AS DESIGNED (SOURCE SHEET 15).

## POST-TENSION TENDON SCHEDULE

(TRANSCRIBED FROM SOURCE - VERIFY)

| GRP | MARK | STR | STRAND NOS. | LENGTH m |
|---|---|---|---|---|
| X / EX DIRECTION | | | | |
| 1 | X8 | 3 | 1-3 | 20.65 |
| 2 | X7 | 4 | 4-7 | 20.15 |
| 3 | X1 | 4 | 8-11 | 21.05 |
| 4 | X1 | 4 | 12-15 | 21.05 |
| 5 | X1 | 4 | 16-19 | 21.05 |
| 6 | X2 | 3 | 20-22 | 36.05 |
| 7 | X2 | 4 | 23-26 | 36.05 |
| 8 | X3 | 4 | 27-30 | 48.90 |
| 9 | X3 | 4 | 31-34 | 48.90 |
| 10 | X3 | 4 | 35-38 | 48.90 |
| 11 | X4 | 4 | 39-42 | 48.25 |
| 12 | X4 | 4 | 43-46 | 48.25 |
| 13 | X5 | 4 | 47-50 | 20.15 |
| 14 | X6 | 3 | 51-53 | 20.65 |
| 58 | EX4 | 3 | 190-192 | 12.95 |
| 59 | EX2 | 3 | 193-195 | 12.95 |
| 60 | EX1 | 3 | 196-198 | 14.85 |
| 61 | EX1 | 2 | 199-200 | 14.85 |
| 62 | EX3 | 2 | 201-202 | 14.90 |
| 63 | EX3 | 3 | 203-205 | 14.90 |
| Y DIRECTION | | | | |
| 15 | Y1 | 4 | 54-57 | 9.45 |
| 16 | Y1A | 4 | 58-61 | 9.25 |
| 17 | Y1A | 4 | 62-65 | 9.25 |
| 18 | Y2 | 4 | 66-69 | 9.00 |
| 19 | Y2 | 3 | 70-72 | 9.00 |
| 20 | Y3 | 2 | 73-74 | 8.95 |
| 21 | Y3 | 2 | 75-76 | 8.95 |
| 22 | Y3 | 2 | 77-78 | 8.95 |
| 23 | Y4 | 2 | 79-80 | 20.75 |
| 24 | Y5 | 4 | 81-84 | 18.10 |
| 25 | Y6 | 4 | 85-88 | 18.60 |
| 26 | Y6 | 4 | 89-92 | 18.60 |
| 27 | Y7 | 4 | 93-96 | 18.10 |
| 28 | Y8 | 2 | 97-98 | 18.40 |
| 29 | Y9 | 2 | 99-100 | 20.70 |
| 30 | Y9A | 2 | 101-102 | 21.20 |
| 31 | Y10 | 4 | 103-106 | 20.70 |
| 32 | Y11 | 4 | 107-110 | 21.70 |
| 33 | Y11 | 4 | 111-114 | 21.70 |
| 34 | Y12 | 4 | 115-118 | 18.70 |
| 35 | Y12 | 2 | 119-120 | 18.70 |
| 36 | Y12 | 2 | 121-122 | 18.70 |
| 37 | Y12 | 2 | 123-124 | 18.70 |
| 38 | Y12 | 4 | 125-128 | 18.70 |
| 39 | Y11 | 4 | 129-132 | 21.70 |
| 40 | Y11 | 4 | 133-136 | 21.70 |
| 41 | Y10 | 4 | 137-140 | 20.70 |
| 42 | Y9A | 2 | 141-142 | 21.20 |
| 43 | Y9 | 2 | 143-144 | 20.70 |
| 44 | Y13 | 2 | 145-146 | 21.25 |
| 45 | Y7 | 4 | 147-150 | 18.10 |
| 46 | Y6 | 4 | 151-154 | 18.60 |
| 47 | Y6 | 4 | 155-158 | 18.60 |
| 48 | Y5 | 4 | 159-162 | 18.10 |
| 49 | Y4 | 2 | 163-164 | 20.75 |
| 50 | Y14 | 2 | 165-166 | 20.75 |
| 51 | Y15 | 2 | 167-168 | 9.45 |
| 52 | Y15 | 2 | 169-170 | 9.45 |
| 53 | Y16 | 3 | 171-173 | 9.50 |
| 54 | Y16 | 4 | 174-177 | 9.50 |
| 55 | Y17A | 4 | 178-181 | 9.75 |
| 56 | Y17A | 4 | 182-185 | 9.75 |
| 57 | Y17 | 4 | 186-189 | 9.95 |

STR: 4 = SQUARE, 3 = TRIANGLE, 2 = CIRCLE
LABEL LENGTH = DRAWN LENGTH + ~0.5 m (SOURCE)